לוח ראשי-בית כנסת

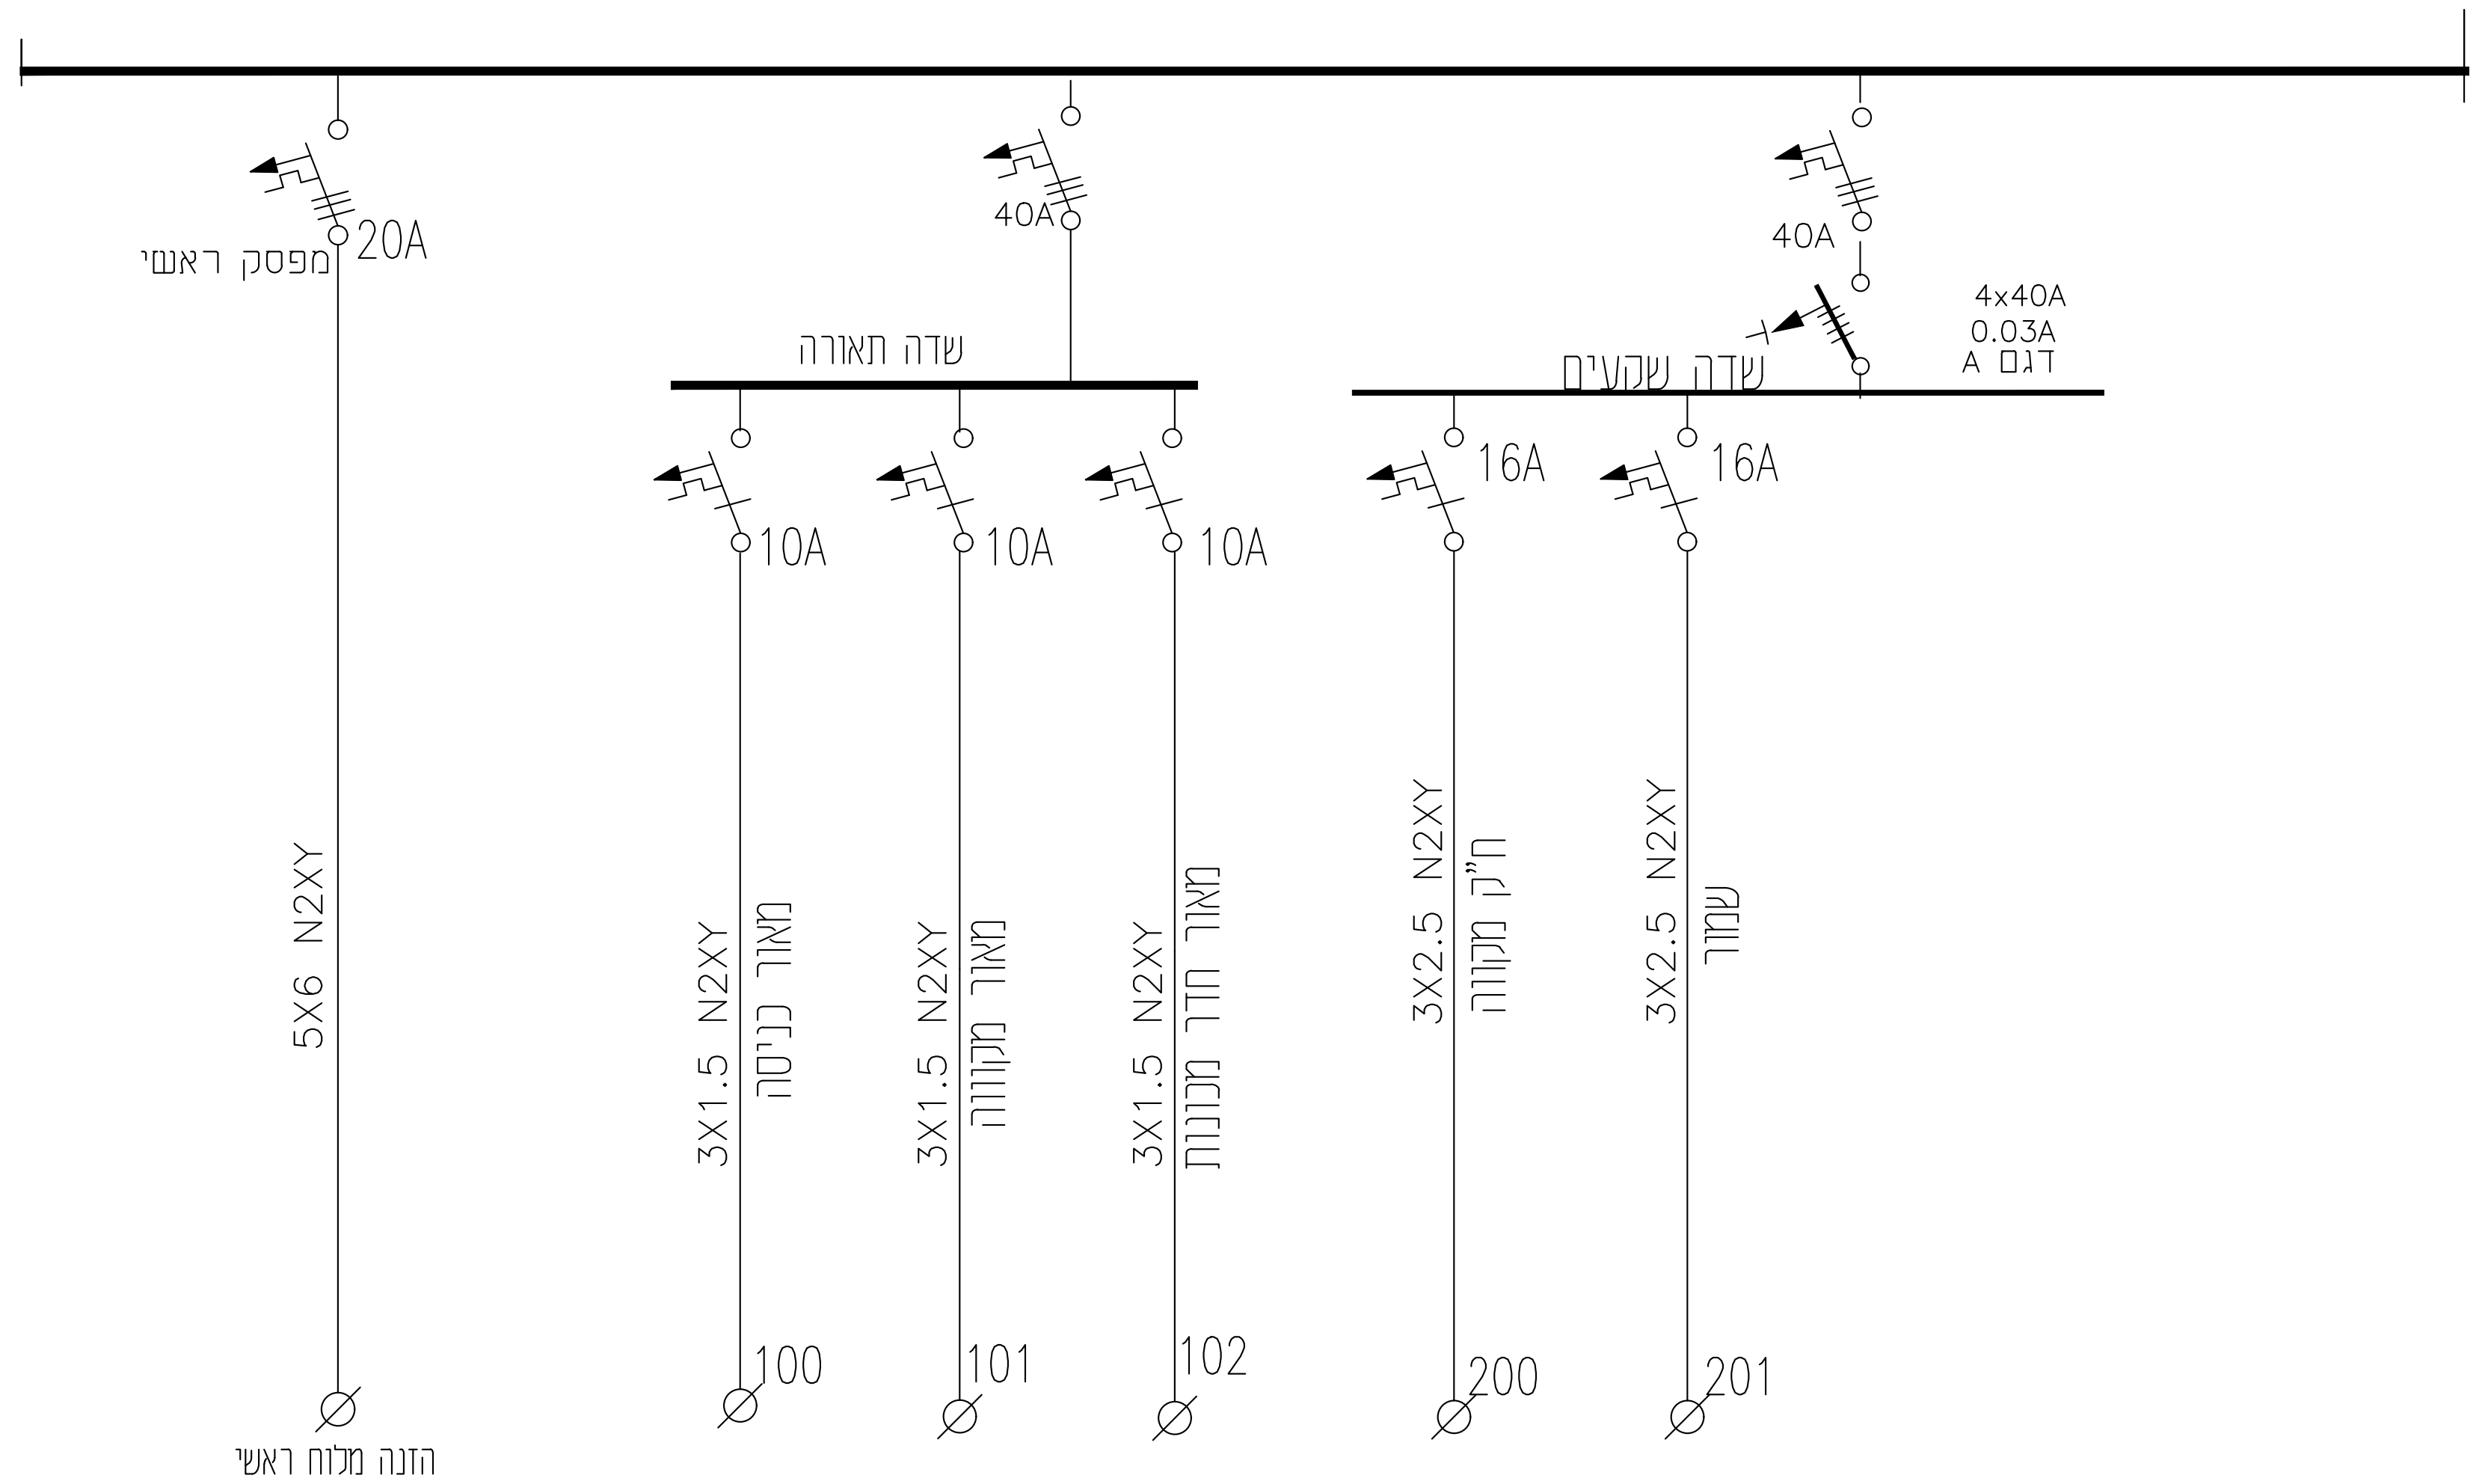

לוח משנה-מקווה

הערות :

1. הכניסות כבלים ללוחות מלמעלה
2. יש להשאיר 30% מקום שמור במבנה הלוחות
3. נדרש לוודא איזון פאזות

מהדורה	תאריך	מהות העידכון
2	17.7.25	לביצוע
1	23.4.25	עדכון עפ"י בטיחות

שם המזמין
מ.א אשקלון

שם הפרויקט
בית כנסת מקווה בבאר גנים

מספר הפרויקט:
25.26.100

מספר גיליון
25.26.100.10

שם גיליון
לוח

קנ"מ: —
תאריך 17.7.25

תכנן איתי-משה אבוקרט
שרטט: ליעד-תהילה ירדני
בדק: איתי-משה אבוקרט

סטטוס: לעיון: ☐ למכרז: ☐ לביצוע: ■

איתי-משה אבוקרט- מהנדס חשמל
מספר רישיון: 1003107
נייד: 050-6926383
E-Mail:itaiabukarat@gmail.com

AVENUE PROJECTS LTD
אבניו פרוייקטים בע"מ
מגדלי M-TOWER
(רח' פריאר 9/604 קומה 6)
טל' פקס: 08-9197861
נייד: 050-9499333
E-Mail:yakir@avenue52.co.il

CERTIFIED ISO 9001:2015 COMPANY