נתוני לוח

מקדם העמסה R.D.F (לפי חישוב)	0.7
תנאי סביבה	רגילים
טמפרטורת סביבה	35°c
זרם קצר צפוי ICP	10KA
זרם קצר מותנה ICC	10KA
הגנה מזרם קצר SCPD	בלוח
זרם של הלוח InA	40A
מתח הפעלה Un=Ue	400V–AC
מתח פיקוד	230V–AC
תדר fn	50Hz
שיטת הארקה	
סביבת עבודה (אלקטרומגניטת)EMC	A(תעשייתי)
דרגת זיהום	3
מתח הבדדה UI(מתח זחילה))	1000V
יכולת עמידה במתח הלם UImP	4KV
הגנה מפני פגיעות מכניות	IK=10
דרגת ההגנה IP	IP–55

מידות

מסד(מבנה)	IEC–62208
יצרן מבנה	Retal
צבע (אלקטרוסטטי)	RAL–7035
מידה כללית HXWXD	800/600/300
משקל מעורר	~ 80kg
דלתות	כן
פנלים	לא
פלטות פח	כן
כניסה כבלים (כניסה ראשית מלמטה)	מלמטה
מידור	FORM–1

שונות

שימוש	פנימי		---
	חיצוני		כן
שיטת התקנה			העמדה על הרצפה
אמצעי הגנה מפני חישמול			ישיר /עקיף
מפעילים			מיומנים בלבד
סוג חיבור	מעגל כניסה ראשי :		F
	מעגל יציאה ראשי :		F
	מעגלי עזר :		F

לוח החשמל מיוצר בהתאם לתקן ישראלי 61439–2

אזהרה!!! התקנה שימוש טיפול ואחזקה של לוח החשמל–ע"י משתמשים מורשים ומוסמכות בלבד

ס.ס לוחות חשמל ובקרה S.S Electrical and control panels ת.ד 3659200 טל: 04–6565394 פקס: 04–8338123 Email: electrcpss@gmail.com	שם הפרויקט : שדה ורבורג	מס תוכנית : 26/952–1	תאריך : 05/10/2026
דף מס': 1 מתוך: 9 קנ"מ: 1:100	שם הלוח: מזמין: מנהרות 1 pro fit agro	מתכנן: מחמוד זועבי שרטט: הבה גמאזנה אישר : עופר אלרון	1: 2: 3: בדק:

מכון התקנים הישראלי

מוליכים:

מוליכי פיקוד	IN	OUT
(AC/DC)	כתום	סגול
כבל אנלוגי מסוכך – אדום / שחור		

מוליכי כח	פאזה	אפס
50/110/230/400 VAC	חום	כחול
נחושת גמישה	שחור	כחול
5/12/24/48 VAC	אפור	לבן

מוליכי DC	L+	L–
5/12/24/48 VAC	אדום	שחור

מהדקים:

מהדקי פיקוד	IN	OUT
כבל אנלוגי מסוכך	אדום / שחור	אדום / שחור
D/I (AC)	כתום	
D/O (AC)	סגול	

מהדקי כח	פאזה	אפס
50/110/230/400 VAC	אפור	כחול

טבלת מומנטים DIN	
מומנט סגירה לפי	סוג בורג לפי
2 Nm	M4
3 Nm	M5
5.5Nm	M6
15 Nm	M8
30 Nm	M10
60 Nm	M12
120 Nm	M16

שלטים לזיהוי מעגלים בלוח:

שדה	צבע כיתוב	צבע רקע
רגיל (בלתי חיוני)	שחור	לבן
חיוני	אדום	לבן
אל – פסק	כחול	לבן
12–48VAC/DC	ירוק	לבן
מפסק ראשי	אדום	לבן

אזהרה !!! התקנה שימוש טיפול ואחזקה של לוח החשמל–ע"י משתמשים מורשים ומוסמכים בלבד

ס.ס לוחות חשמל ובקרה
S.S Electrical and control panels
ת.ד 3659200 276 טל: 04–6565394 פקס: 04–8338123
Email: electrcpss@gmail.com

מערכת ניהול איכות מאושרת ISO 9001: 2008
מכון התקנים הישראלי

שם הפרויקט : שדה ורבורג		מס תוכנית: 26/952–1	תאריך: 05/10/2026
שם הלוח: מנהרות 1	דף מס': 2	מתכנן: מחמוד זועבי	1:
מזמין: pro fit agro	מתוך: 9	שרטט: הבה גמאחנה	2:
	קנ"מ: 1:100	אישר: עופר אלרון	3:
			בדק:

דוגמה לצבעי בידוד מוליכים ומהדקים בלוח

מערכת	תפקיד	צבע		
		צבע בידוד	פסים גמישים	צבע מהדק
AC-230/400V	תלת פאזי L1			אפור או באז'
	תלת פאזי L2			אפור או באז'
	תלת פאזי L3			אפור או באז'
	Netural (N)			כחול
	Protective earth (PE)		כולל סימון על הבידוד	
AC 12-48 V	תלת פאזי L			
	Netural (N)			
AC 50-230 V	תלת פאזי L			אפור או באז'
	Netural (N)			כחול
DC 12-48 V	מוליך (+)			
	מוליך (-)			

תאריך: 05/10/2026	מס תוכנית: 26/952-1	שם הפרויקט: שדה ורבורג	ס.ס לוחות חשמל ובקרה S.S Electrical and control panels ת.ד 3659200 טל: 04-6565394 פקס: 04-8338123 Email: electrcpss@gmail.com
1:	מתכנן: מחמוד זועבי	שם הלוח: מנהרות 1 מזמין: pro fit agro	דף מס': 3 מתוך: 9 קנ"מ: 1:100
2:	שרטט: הבה גמאחנה		
3:	אישר: עופר אלרון		
בדק:			


מערכת ניהול איכות מאושרת ת"י ISO 9001: 2008
מכון התקנים הישראלי


מנהרות 1

מס תוכנית: 26/952-1
תאריך יצור: ----------

מיוצר בהתאם לתקן
ישראלי 61439-2

ס.ס. לוחות חשמל ובקרה
טל: 04-6565394
פקס: 04-8338123
כתובת: אבטין 3659200 ת.ד. 276

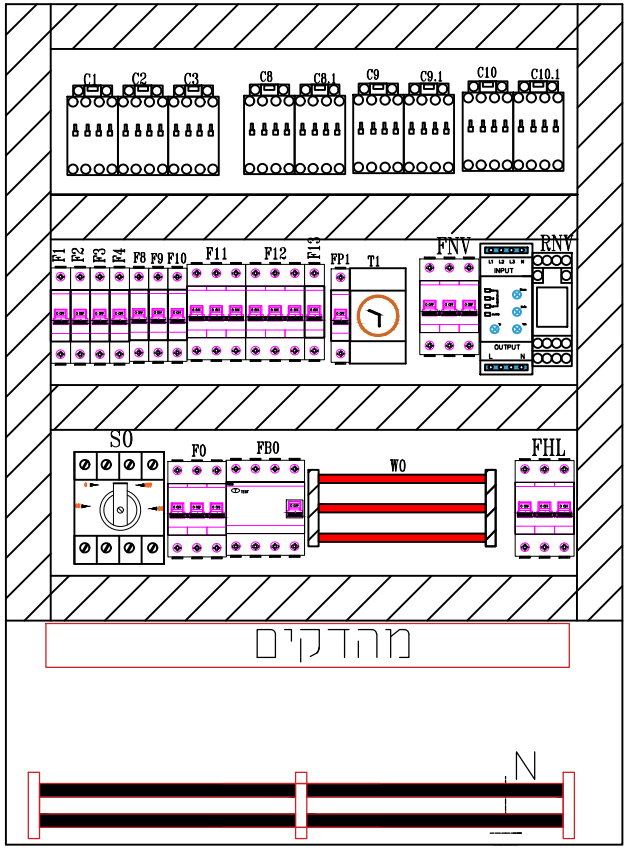


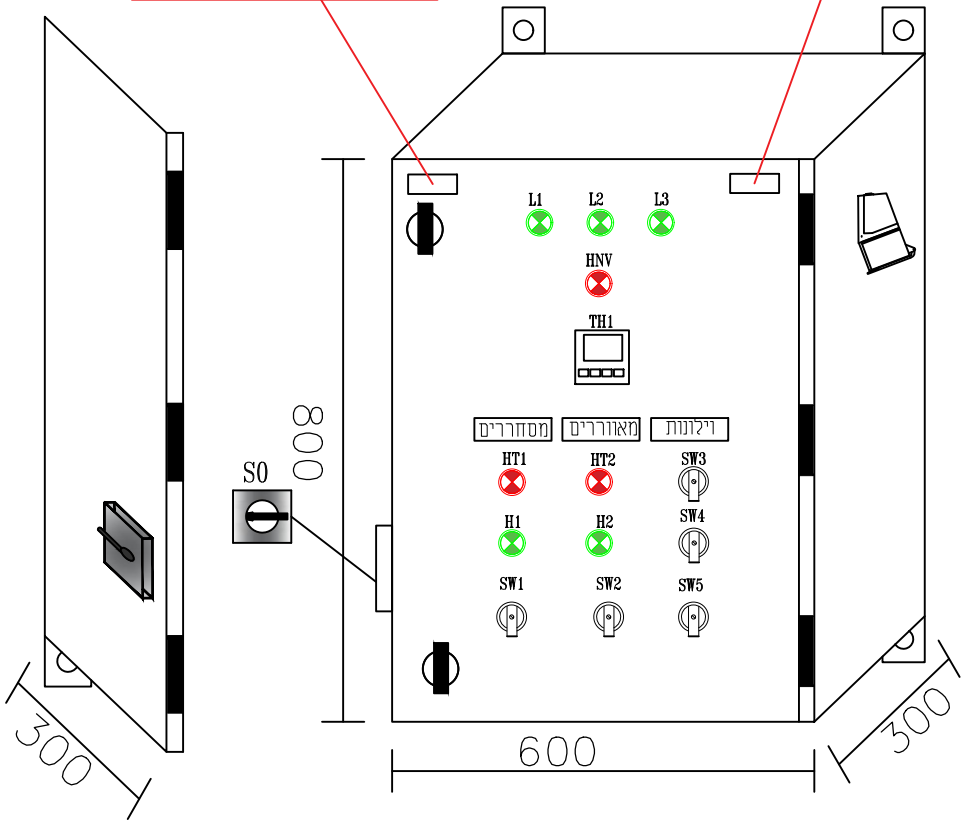

תאריך: 05/10/2026	מס תוכנית: 26/952-1	שם הפרויקט: שדה ורבורג	
1:	מתכנן: מחמוד זועבי	שם הלוח: מנהרות 1	דף מס': 4
2:	שרטט: הבה גמאחנה	מזמין: pro fit agro	מתוך: 9
3:	אישר: עופר אלרון		קנ"מ: 1:100
בדק:			


ס.ס לוחות חשמל ובקרה
S.S Electrical and control panels
ת.ד 3659200 276 טל: 04-6565394 פקס: 04-8338123
Email: electrcpss@gmail.com

מערכת ניהול איכות מאושרת
ISO 9001: 2008
מכון התקנים הישראלי

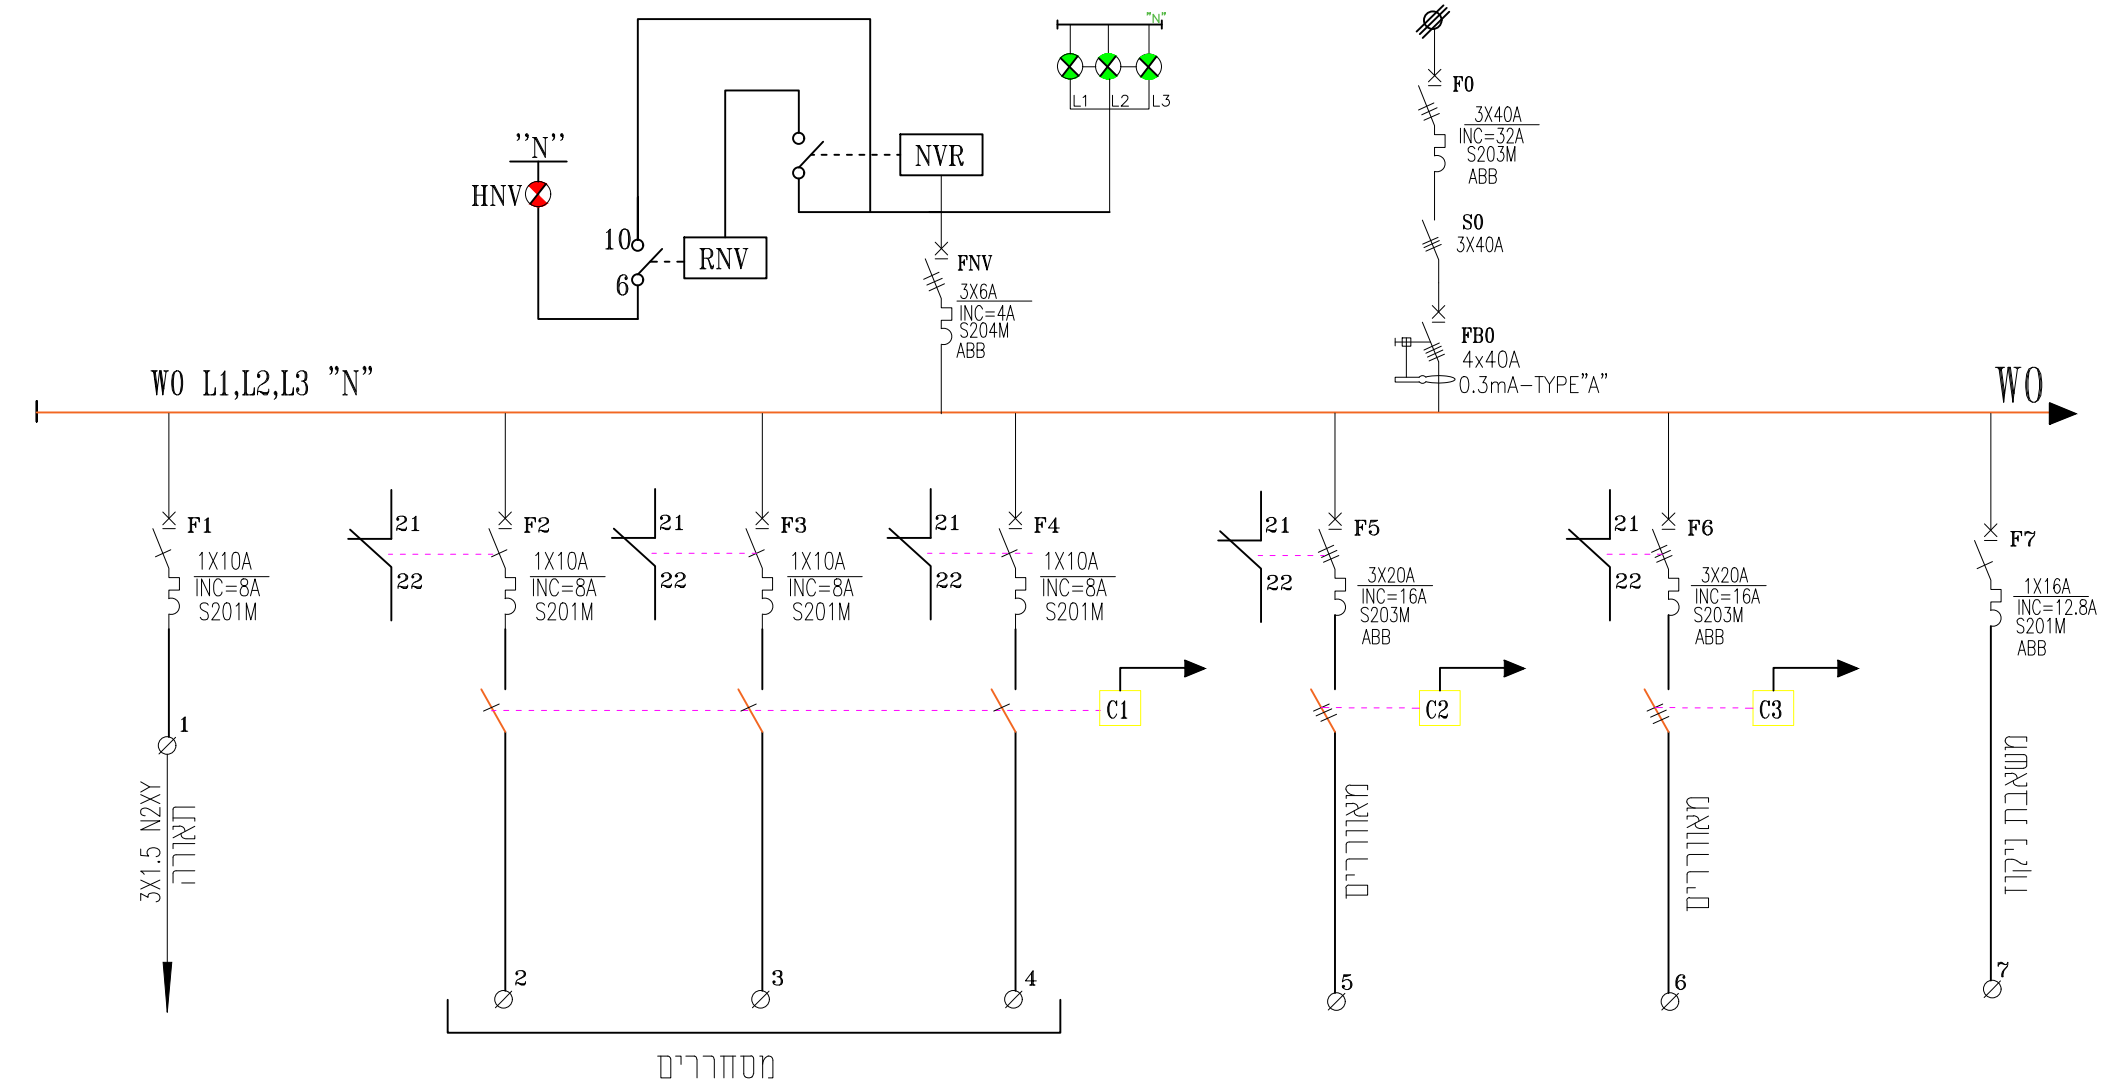


תאריך: 05/10/2026	מס תוכנית: 26/952-1	שם הפרויקט: שדה ורבורג	ס.ס לוחות חשמל ובקרה S.S Electrical and control panels ת.ד 3659200 276 טל: 04-6565394 פקס: 04-8338123 Email: electrcpss@gmail.com
1:	מתכנן: מחמוד זועבי	שם הלוח: מנהרות 1	דף מס': 5
2:	שרטט: הבה גמאחנה	מזמין: pro fit agro	מתוך: 9
3:	אישר: עופר אלרון		קנ"מ: 1:100
בדק:			

מערכת ניהול איכות מאושרת ת"י ISO 9001: 2008
מכון התקנים הישראלי

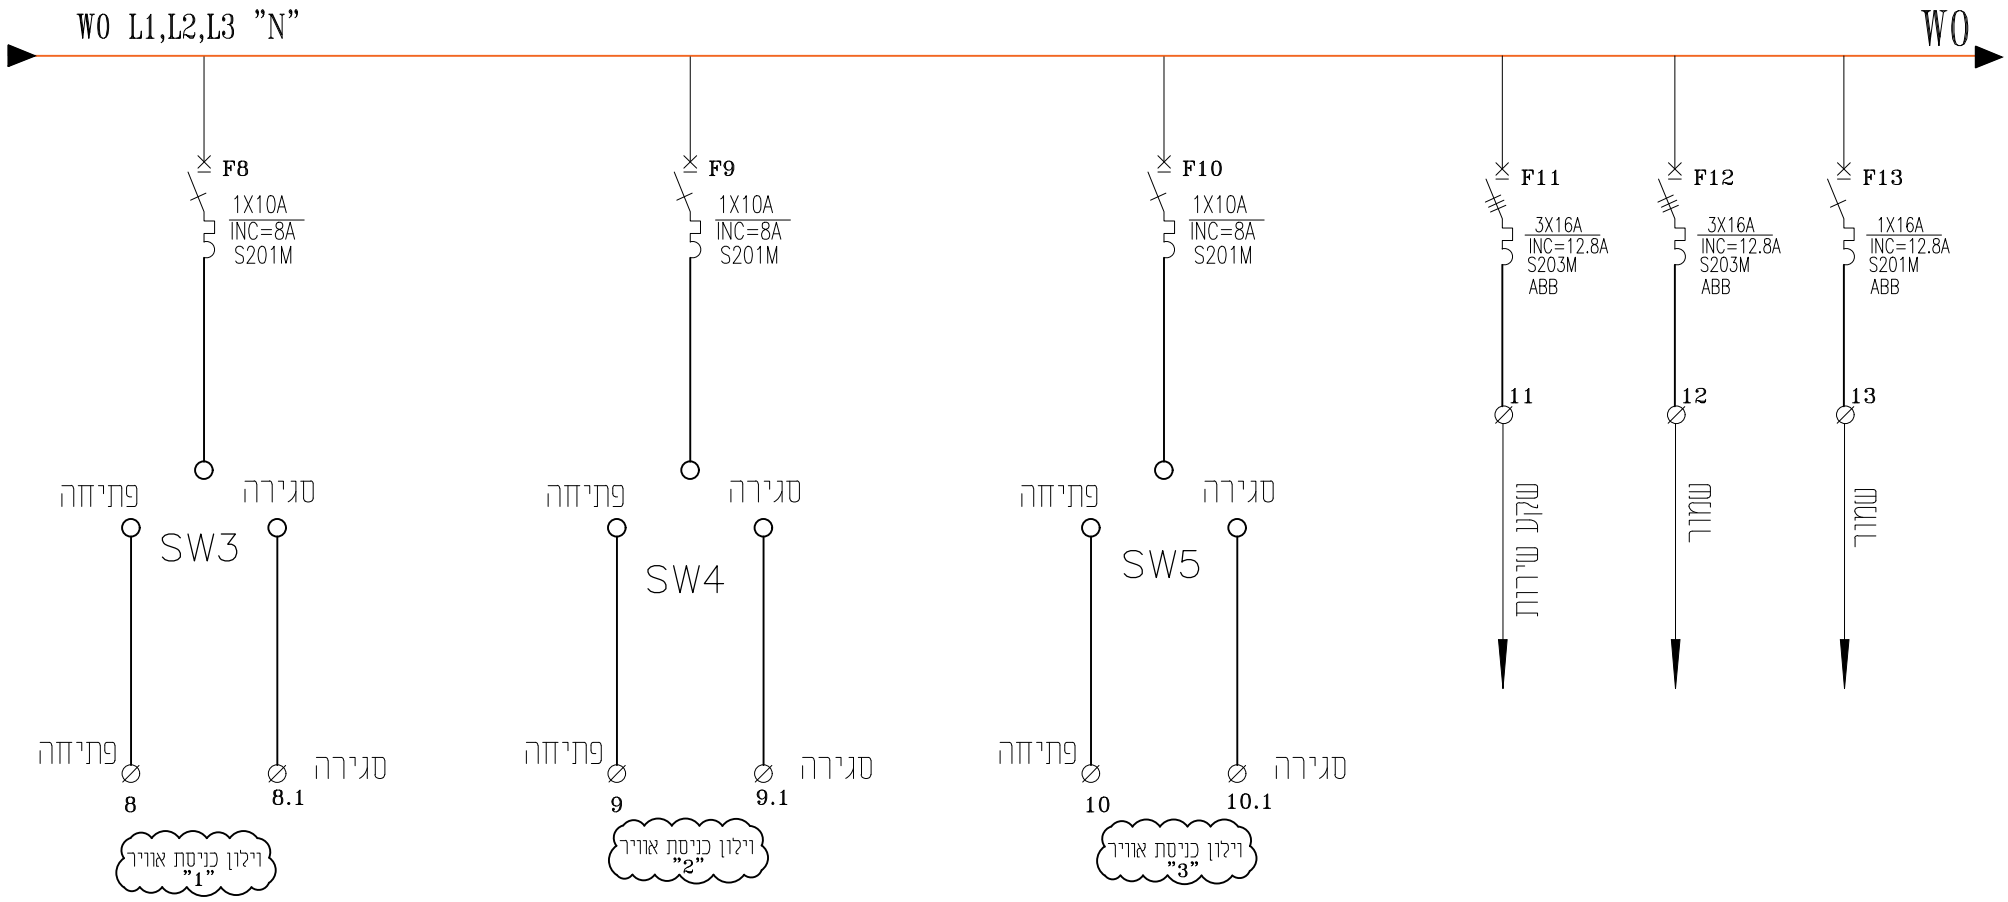


תאריך: 05/10/2026	מס תוכנית: 26/952-1	שם הפרויקט: שדה ורבורג	ס.ס לוחות חשמל ובקרה S.S Electrical and control panels 04-8338123: פקס 04-6565394: טל 276 ת"ד 3659200 Email: electrcpss@gmail.com
1:	מתכנן: מחמוד זועבי	שם הלוח: מנהרות 1	דף מס': 6
2:	שרטט: הבה גמאחנה	מזמין: pro fit agro	מתוך: 9
3:	אישר: עופר אלרון		קנ"מ: 1:100
בדק:			

מערכת ניהול איכות מאושרת ת"י ISO 9001: 2008
מכון התקנים הישראלי

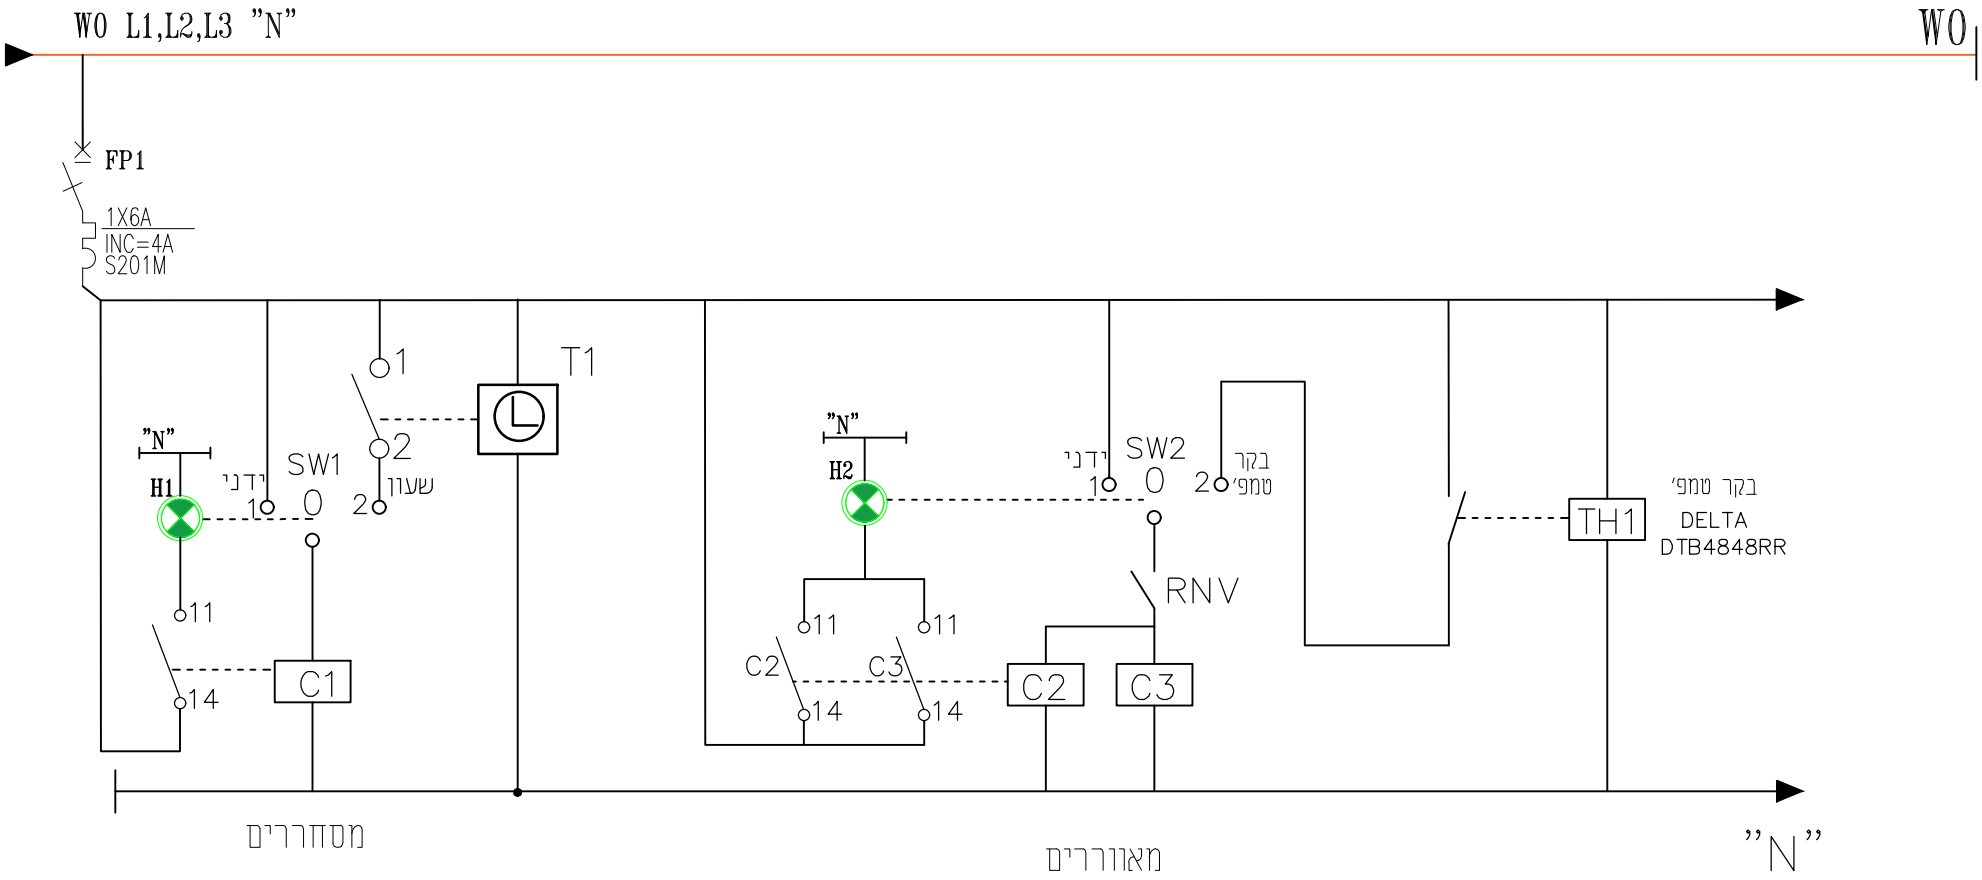

תאריך: 05/10/2026	מס תוכנית: 26/952-1	שם הפרויקט: שדה ורבורג	ס.ס לוחות חשמל ובקרה S.S Electrical and control panels ת.ד 3659200 רח' 276 טל: 04-6565394 פקס: 04-8338123 Email: electrcpss@gmail.com
1:	מתכנן: מחמוד זועבי	שם הלוח: מנהרות 1	דף מס': 7
2:	שרטט: הבה גמאחנה	מזמין: pro fit agro	קנ"מ: 1:100
3:	אישר: עופר אלרון		
בדק:			

מערכת ניהול איכות מאושרת ISO 9001:2008
מכון התקנים הישראלי

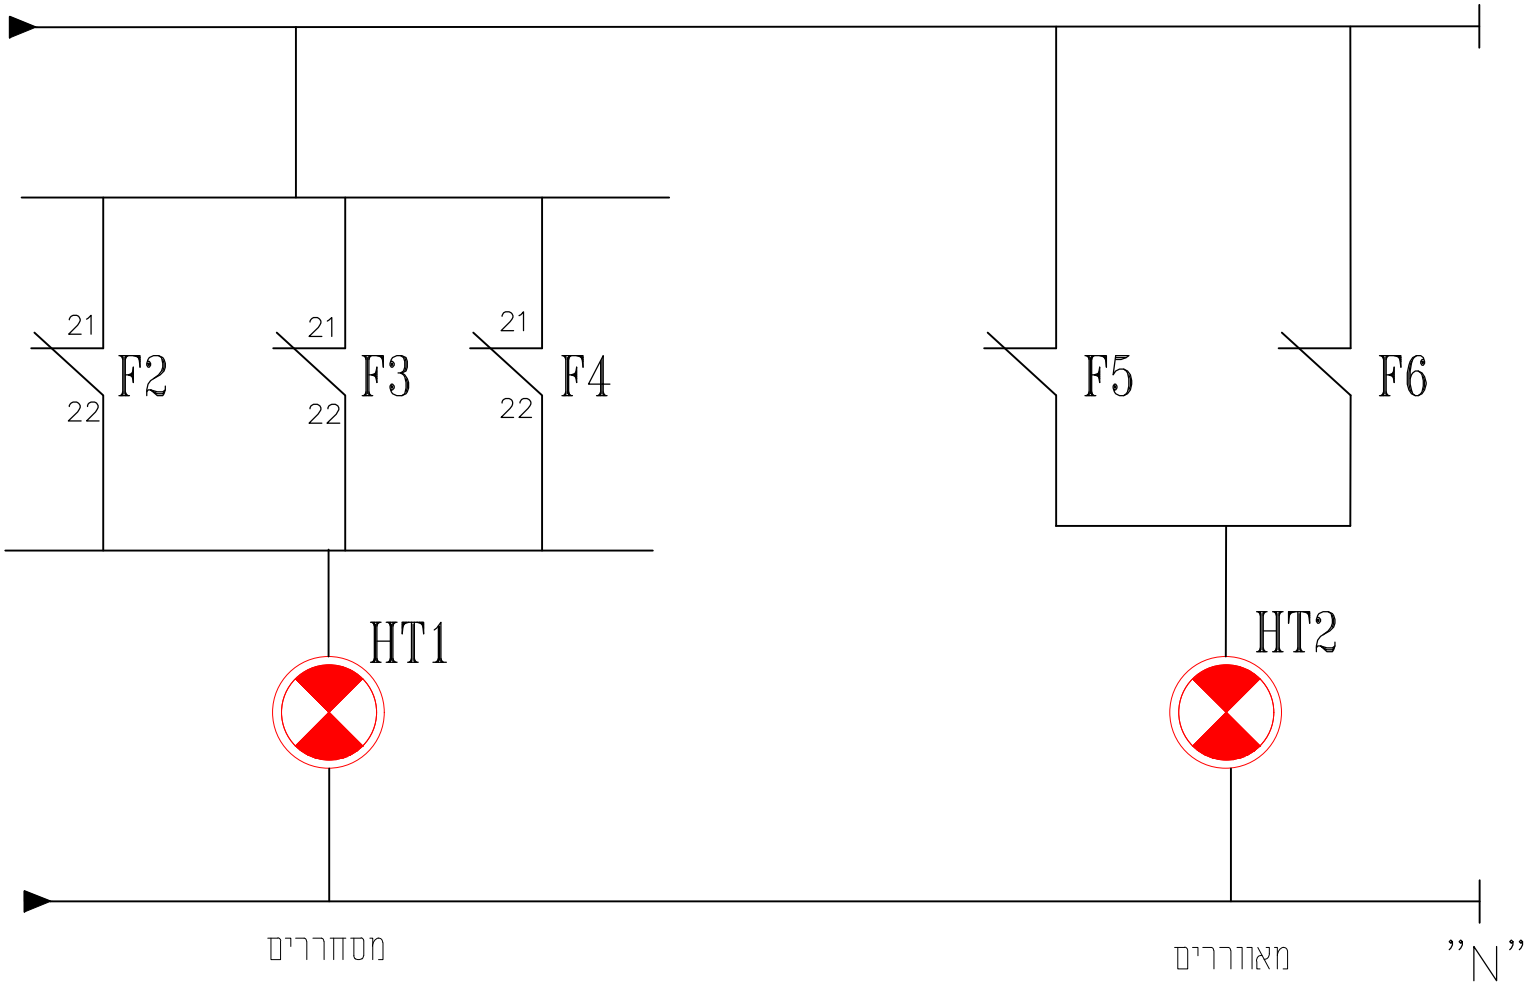

תאריך: 05/10/2026	מס תוכנית: 26/952-1	שם הפרויקט: שדה ורבורג	ס.ס לוחות חשמל ובקרה S.S Electrical and control panels ת.ד 3659200 רח' 276 טל: 04-6565394 פקס: 04-8338123 Email: electrcpss@gmail.com
1:	מתכנן: מחמוד זועבי	שם הלוח: מנהרות 1	דף מס': 8
2:	שרטט: הבה גמאחנה	מזמין: pro fit agro	קנ"מ: 1:100
3:	אישר: עופר אלרון		
בדק:			

מערכת ניהול איכות מאושרת ISO 9001:2008
מכון התקנים הישראלי