סכמת הזנות

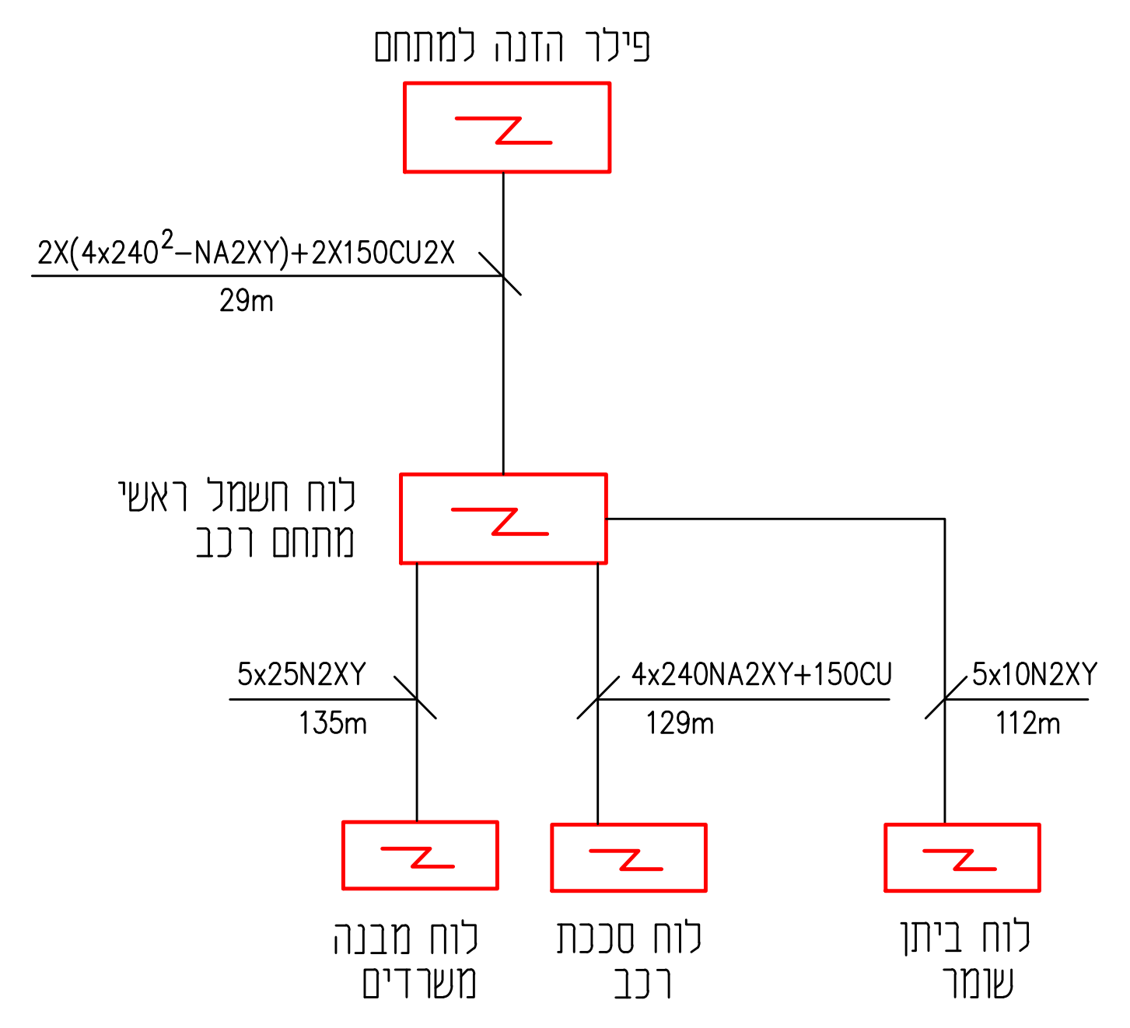
פילר הזנה למתחם
2X(4x240^2–NA2XY)+2X150CU2X
29m
לוח חשמל ראשי מתחם רכב
5x25N2XY
135m
4x240NA2XY+150CU
129m
5x10N2XY
112m
לוח מבנה משרדים
לוח סככת רכב
לוח ביתן שומר

לוח ביתן שומר

לוח במבנה פולקרבונט 850 מעלות 24 ח"א
עה"ט כולל דלת
כל המאז"ים יהיו לזרם קצר 10KA לפי IEC60898
נדרש 30% מקום שמור בלוח

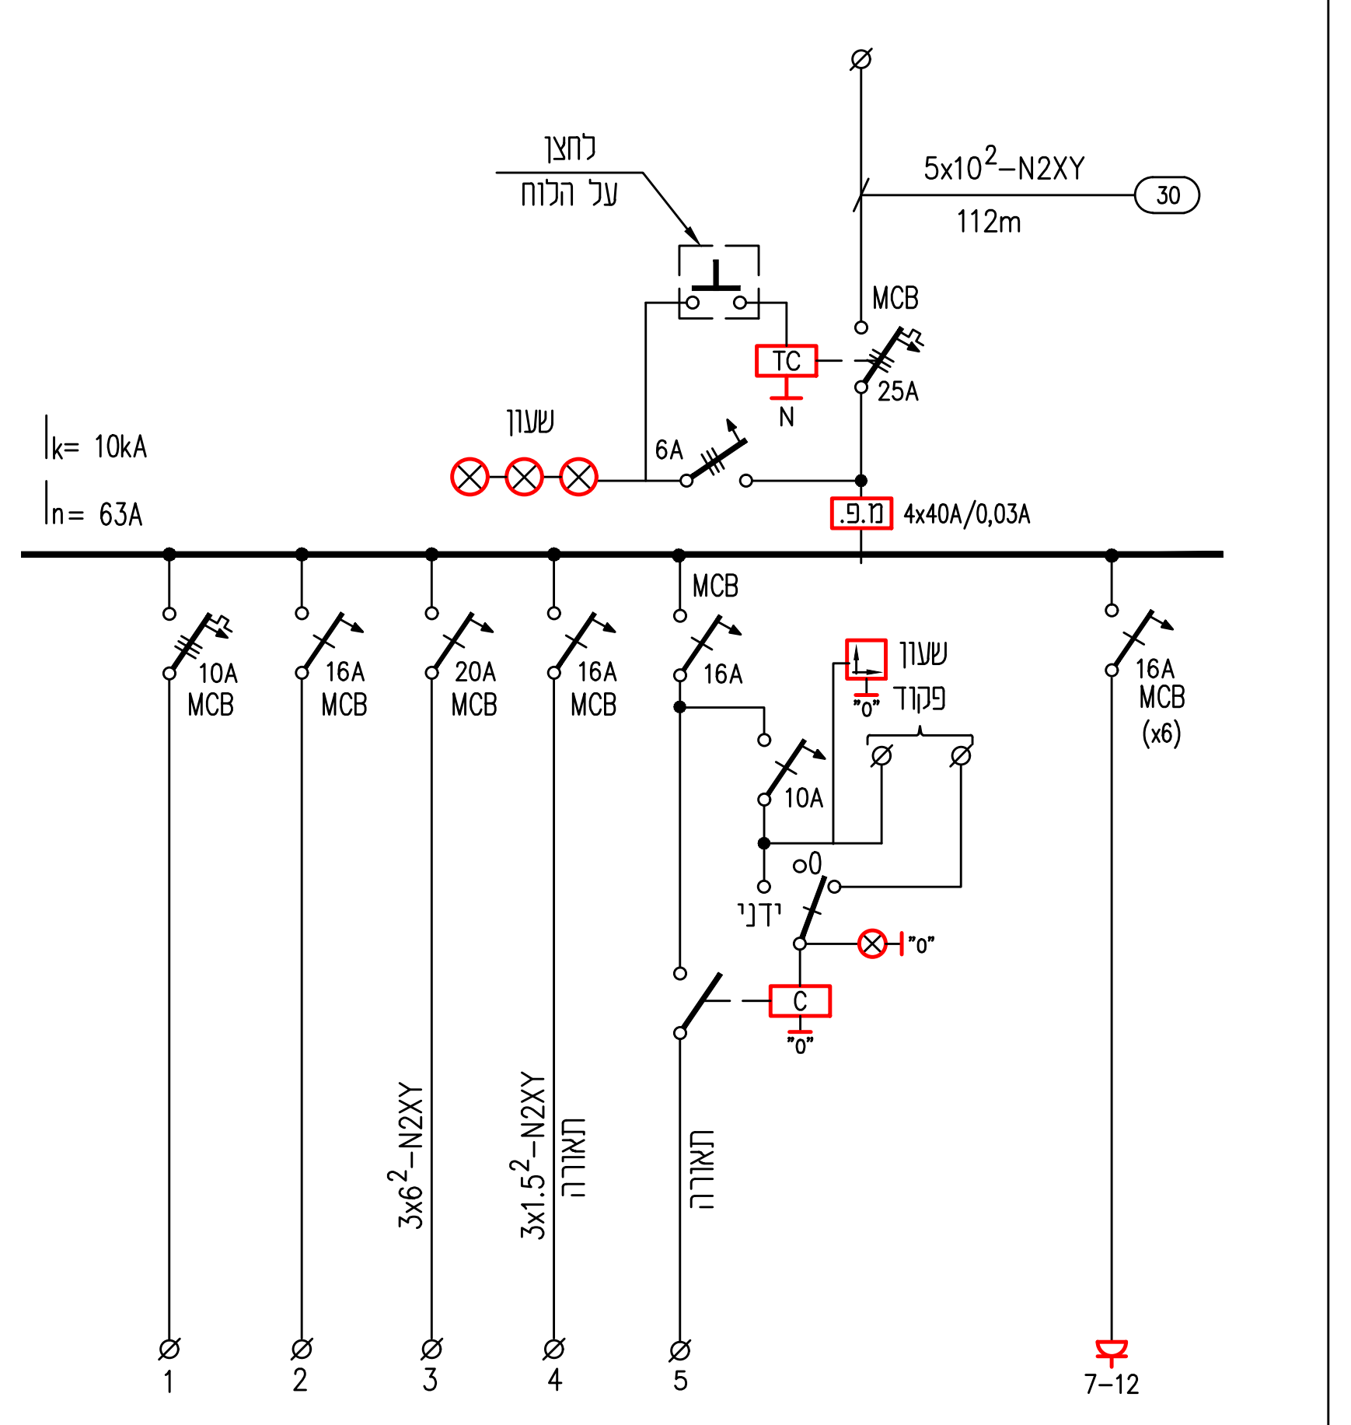
לחצן על הלוח
5x10^2–N2XY
30
112m
MCB
TC
N
25A
שעון
6A
I_k= 10kA
I_n= 63A
מ.פ. 4x40A/0,03A
10A MCB
16A MCB
20A MCB
16A MCB
MCB 16A
שעון פקוד
10A
ידני
"0"
C
16A MCB (x6)
3x6^2–N2XY
3x1.5^2–N2XY תאורה
תאורה
1
2
3
4
5
7–12

לוח סככה

לוח במבנה פח כולל דלת
ופנלים במידות 2.1x1.2x0.5 מטר
כניסה כבלים מלמטה
יציאת כבלים מלמעלה
לוח מיוצר לפי תקן 61439-2
מידור FORM 2B
טמ"פ סביבה – 35C°
דרגת הגנה מכנית IK10
כל המאז"ים יהיו לזרם קצר 10KA לפי IEC60898
נדרש 30% מקום שמור בלוח
חישוב חום ע"י יצרן הלוח בהתאם לציוד המותקן

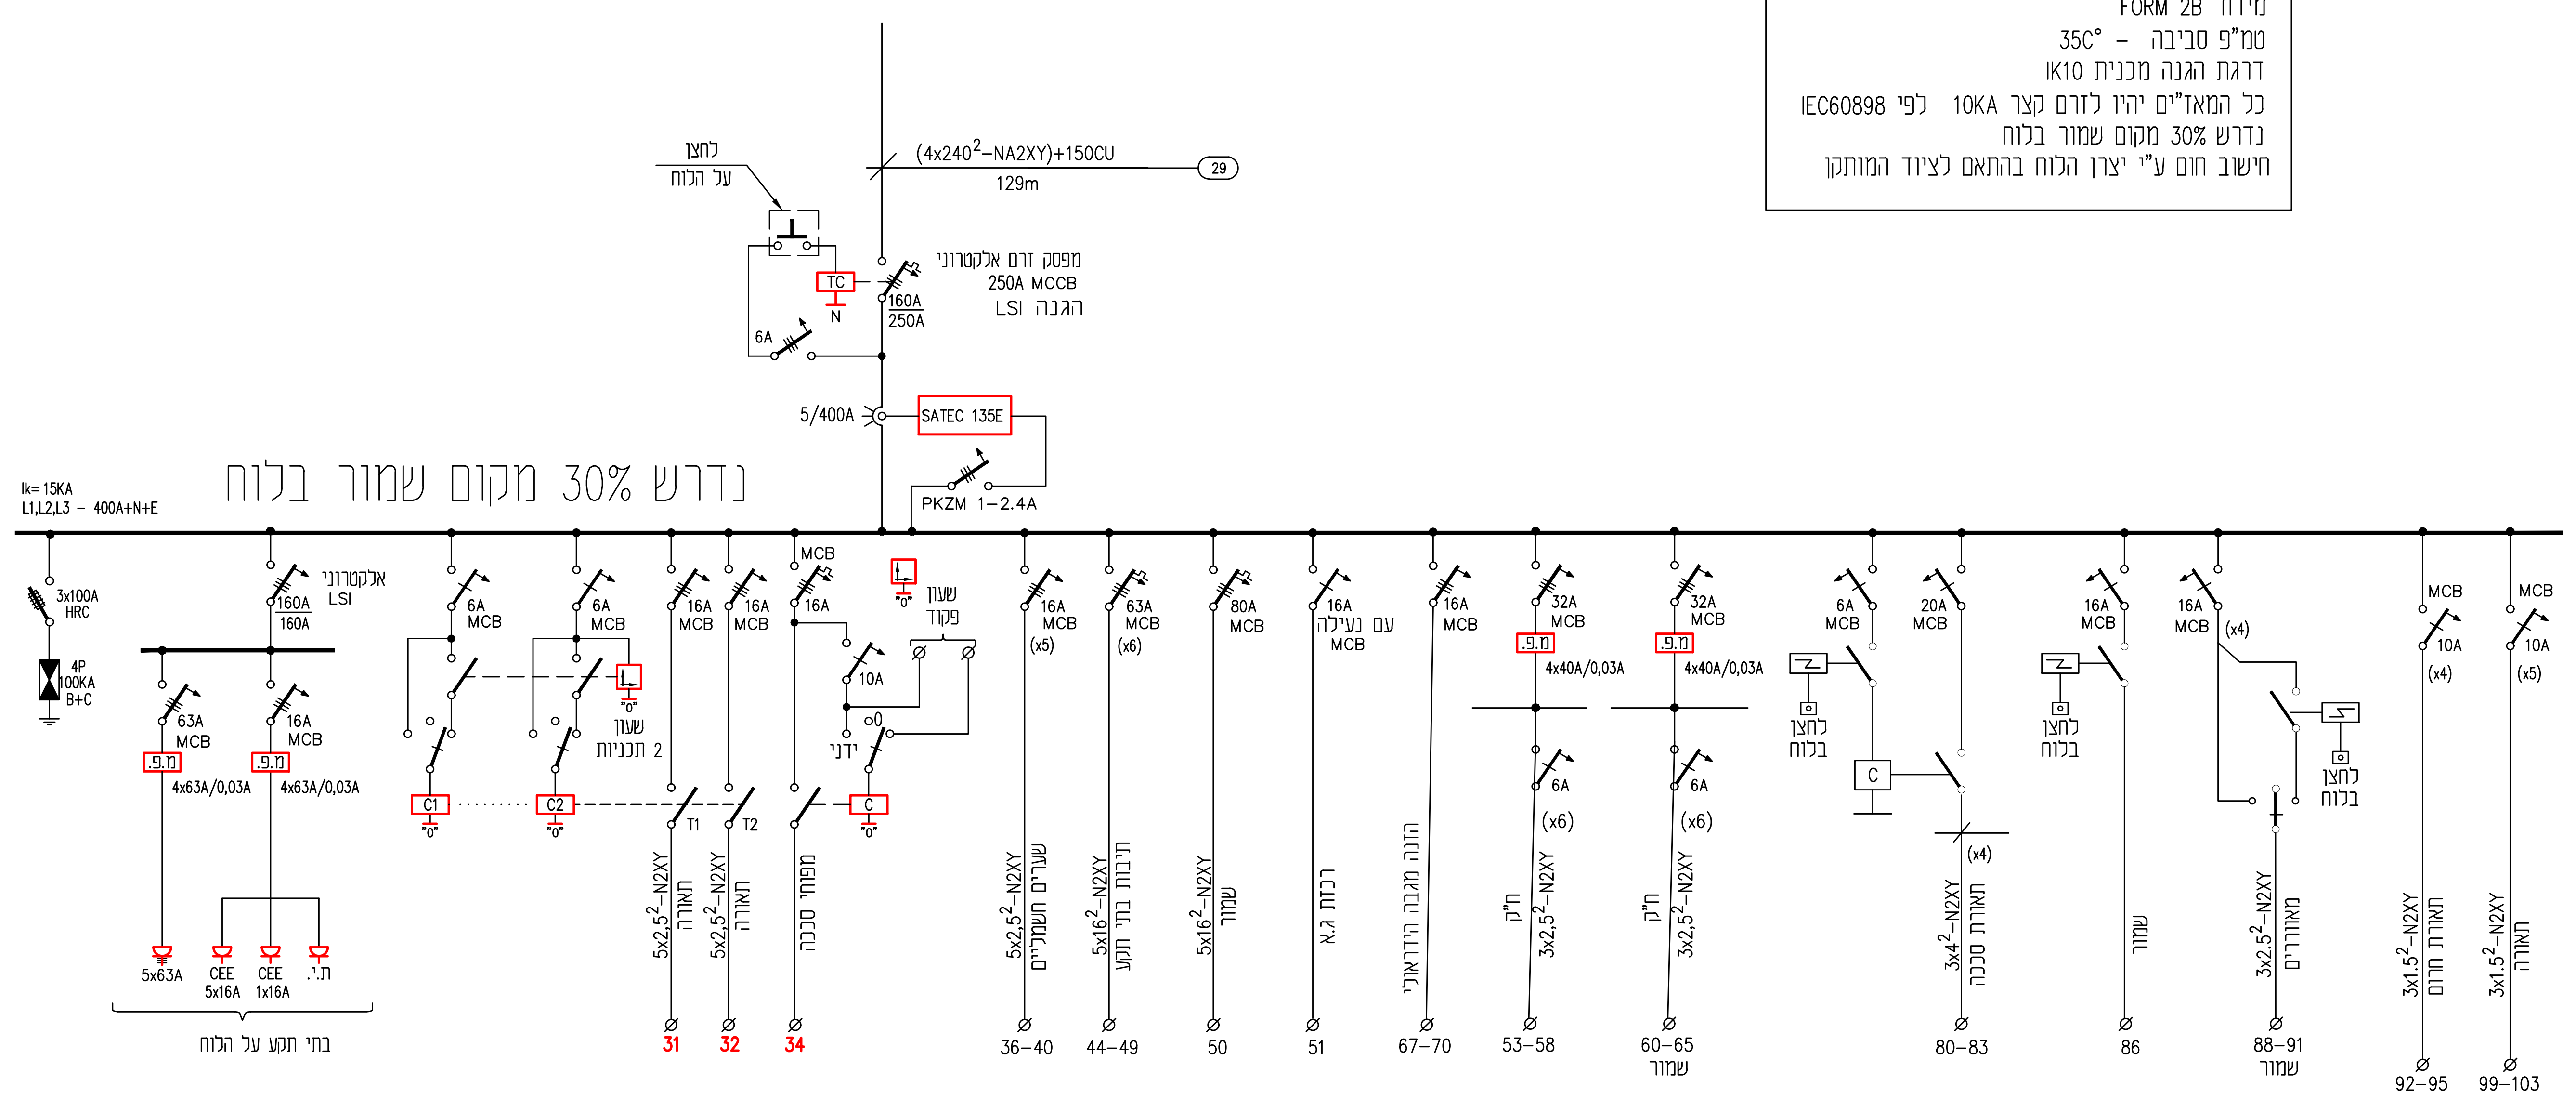
לחצן על הלוח
(4x240^2–NA2XY)+150CU
129m
29
מפסק זרם אלקטרוני 250A MCCB הגנה LSI
TC
N
160A
250A
6A
5/400A
SATEC 135E
PKZM 1–2.4A
נדרש 30% מקום שמור בלוח
Ik= 15KA
L1,L2,L3 – 400A+N+E
3x100A HRC
4P 100KA B+C
אלקטרוני LSI
160A
160A
63A MCB
16A MCB
מ.פ. 4x63A/0,03A
מ.פ. 4x63A/0,03A
5x63A
CEE 5x16A
CEE 1x16A
ת.י.
בתי תקע על הלוח
6A MCB
6A MCB
שעון תכניות 2
C1
C2
"0"
16A MCB
16A MCB
T1
T2
MCB 16A
10A
שעון פקוד
ידני
C
5x2,5^2–N2XY תאורה
5x2,5^2–N2XY תאורה
מפוחי סככה
31
32
34
16A MCB (x5)
5x2,5^2–N2XY שערים חשמליים
36–40
63A MCB (x6)
5x16^2–N2XY תיבות בתי תקע
44–49
80A MCB
5x16^2–N2XY שמור
50
16A MCB עם נעילה
רכזת ג.א
51
16A MCB
הזנה מגבה הידראולי
67–70
32A MCB
מ.פ. 4x40A/0,03A
6A (x6)
3x2,5^2–N2XY ח"ן
53–58
32A MCB
מ.פ. 4x40A/0,03A
6A (x6)
3x2,5^2–N2XY ח"ן
60–65 שמור
6A MCB
לחצן בלוח
C
20A MCB
(x4)
3x4^2–N2XY תאורת סככה
80–83
16A MCB
לחצן בלוח
שמור
86
16A MCB (x4)
לחצן בלוח
3x2.5^2–N2XY מאווררים
88–91 שמור
MCB 10A (x4)
3x1.5^2–N2XY תאורת חרום
92–95
MCB 10A (x5)
3x1.5^2–N2XY תאורה
99–103

לוח ראשי בגומחת בטון ליד היציאה מהמתחם

מבנה לוח פוליאסטר גודל 2
פוליאסטר משוריין
מוגן מים IP65
במידות 1250x1115x320 מ"מ
לוח מיוצר לפי תקן 61439-2
מידור FORM 2B
טמ"פ סביבה – 40C°
נדרש 30% מקום שמור בלוח

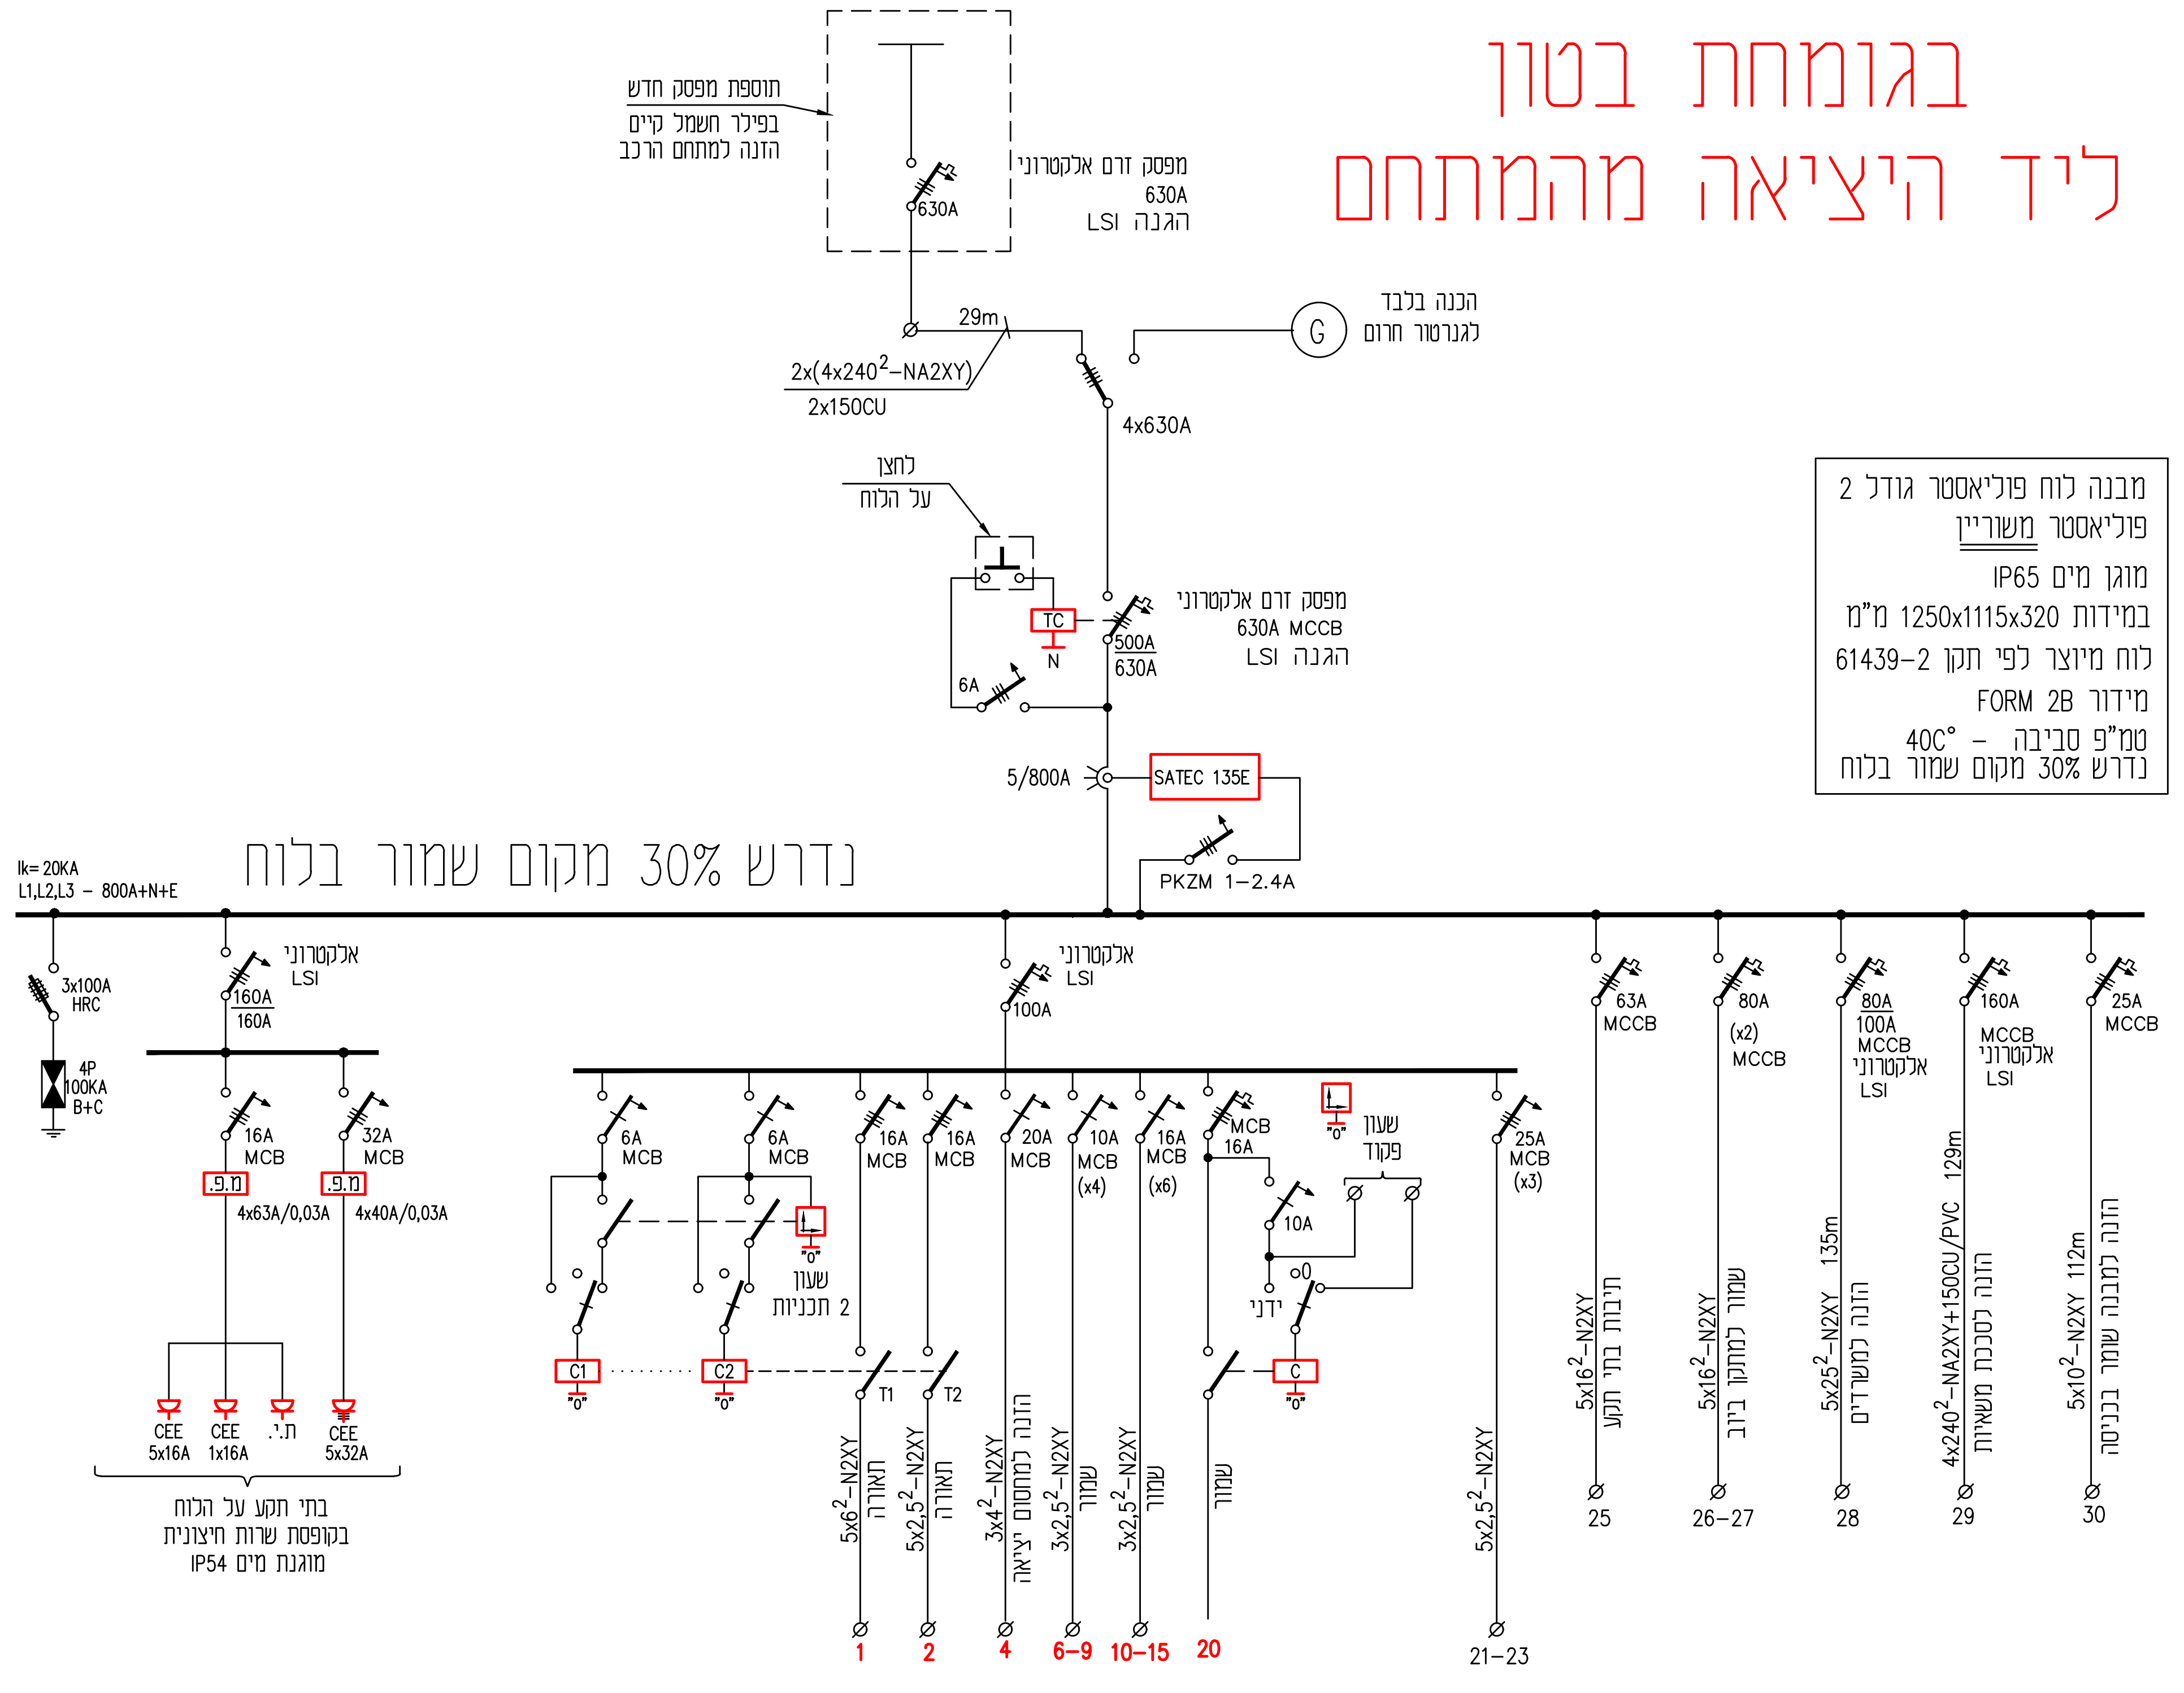
תוספת מפסק חדש בפילר חשמל קיים הזנה למתחם הרכב
630A
מפסק זרם אלקטרוני 630A הגנה LSI
29m
2x(4x240^2–NA2XY)
2x150CU
הכנה בלבד לגנרטור חרום
G
4x630A
לחצן על הלוח
TC
N
6A
500A
630A
מפסק זרם אלקטרוני 630A MCCB הגנה LSI
5/800A
SATEC 135E
PKZM 1–2.4A
נדרש 30% מקום שמור בלוח
Ik= 20KA
L1,L2,L3 – 800A+N+E
3x100A HRC
4P 100KA B+C
אלקטרוני LSI
160A
160A
16A MCB
32A MCB
מ.פ. 4x63A/0,03A
מ.פ. 4x40A/0,03A
CEE 5x16A
CEE 1x16A
ת.י.
CEE 5x32A
בתי תקע על הלוח בקופסת שרות חיצונית מוגנת מים IP54
אלקטרוני LSI
100A
6A MCB
6A MCB
שעון תכניות 2
C1
C2
"0"
16A MCB
16A MCB
T1
T2
20A MCB
10A MCB (x4)
16A MCB (x6)
MCB 16A
10A
ידני
C
שעון פקוד
25A MCB (x3)
5x6^2–N2XY תאורה
5x2,5^2–N2XY תאורה
3x4^2–N2XY הזנה למחסום יציאה
3x2,5^2–N2XY שמור
3x2,5^2–N2XY שמור
שמור
5x2,5^2–N2XY
1
2
4
6–9
10–15
20
21–23
63A MCCB
5x16^2–N2XY תיבות בתי תקע
25
80A (x2) MCCB
5x16^2–N2XY שמור למתקן ביוב
26–27
80A 100A MCCB אלקטרוני LSI
5x25^2–N2XY 135m הזנה למשרדים
28
160A MCCB אלקטרוני LSI
4x240^2–NA2XY+150CU/PVC 129m הזנה לסככת משאיות
29
25A MCCB
5x10^2–N2XY 112m הזנה למבנה שומר בכניסה
30

תפוצה
Distribution

מס. No.	שנויים ותוספות Revisions	תאריך Date
6	שינוי סטטוס לביצוע	12.02.26
5	עדכון	09.02.26
4	עדכון	01.02.26
3	עדכון	11.01.26
2	עדכון	24.08.25
1	עדכון	18.08.25

LIGHTING & ELECTRICAL ENGINEERING CONSULTANTS
ייעוץ ותכנון מתקני חשמל ותאורה
RAMOR LTD. רמאור בע"מ
TEL-AVIV תל - אביב
14 Prof. Shore St. רח' פרופ' שור 14
Tel. No. 03-6052170 טל.
Fax. No. 03-5442737 פקס
E-MAIL ADDRESS carola@ramor.co.il דואר אלקטרוני

JOB NAME **חצרים** שם הפרויקט
DRAWING NAME **תכנית לוחות חשמל** נושא התכנית
DRAWING NO. **6199–2–50** מספר התכנית

אושר	שמואל	30.07.25			שמואל	12.02.26	Approved by:
בוצע	זיו	30.07.25			זיו	12.02.26	Done by:
Rev. No. 6 מהדורה	שם Name	תאריך Date	שם Name	תאריך Date	שם Name	תאריך Date	קנ"מ –– SCALE Do Not scale drawing
	לעיון Info Only ○		למכרז Bidding ○		לבצוע Operative ●		

המבצע אחראי לבדיקת המידות ולהתאמתן במקום.
עליו להודיע למתכנן/מפקח על כל אי-התאמה
ולקבל הנחיותיו בכתב בטרם ימשיך בעבודה.

File Name: שם קובץ: P\PROJECTS-2013\5712-ALON\5712-03
Sheet Size: מידות הגליון ס"מ 90.0 x 55.0 Cm.